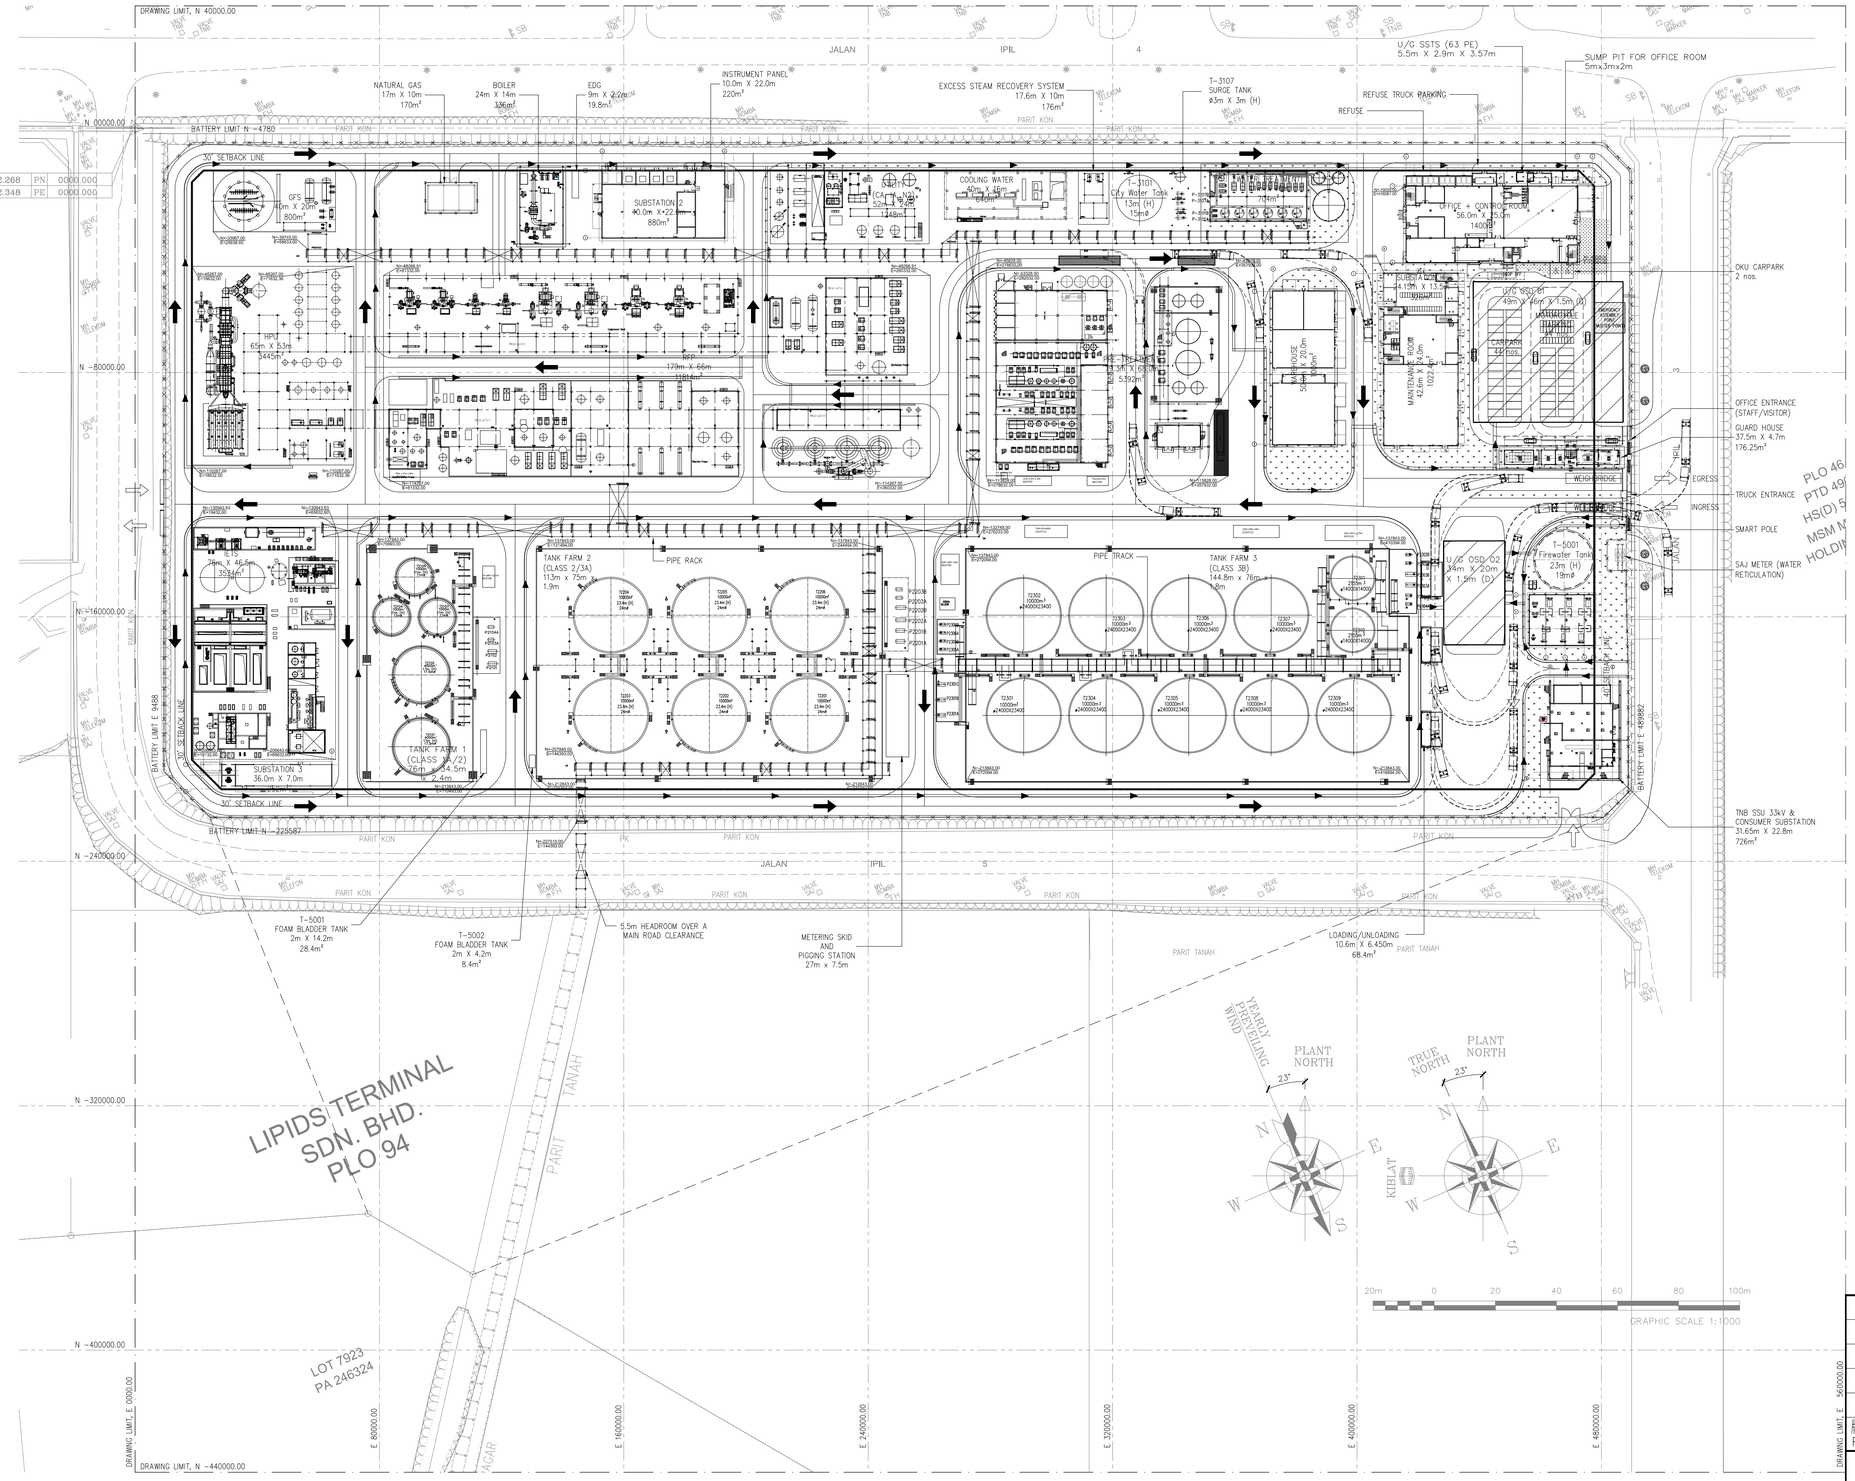

KEYPLAN:

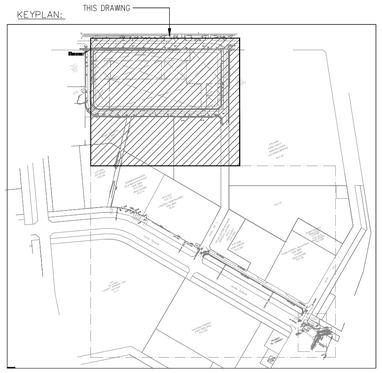

HOLD

1 –

AREA LIST:

DESCRIPTION	UNIT	SIZE
PLOT/GRADING/EARTH WORK PLAN SITE	110	
ROAD AND PAVING	120	
FENCE AND GATE	130	
GUARD HOUSE	140	37.68m X 4.7m
WEIGHBRIDGE	150	18.0m X 3.4m
WAREHOUSE	160	50.0m X 20.0m
MAINTENANCE BUILDING	170	42.6m X 24.0m
OFFICE BUILDING AND CONTROL ROOM	180	61.0m X 25.0m
REFUSE BUILDING	190	
TANK FARM 1 (CLASS 1A/2)	210	76.0m X 34.5m X 2.4m (H)
TANK FARM 2 (CLASS 2/3A)	220	113.0m X 75.0m X 1.9m (H)
TANK FARM 3 (CLASS 3B)	230	144.8m X 76.0m X 1.8m (H)
LOADING/UNLOADING GANTRY	240	10.6m X 6.45m
INTERCONNECTING PIPELINE	250	
WATER TREATMENT SYSTEM (INCLUDE SURGE TANK AND CITY WATER TANK)	310	40.0m X 16.0m
		ø3.0m X 3.0m (H)
		ø15.0m X 13.0m (H)
STEAM BOILER SYSTEM	320	24.0m X 14.0m
COOLING WATER SYSTEM	330	44.0m X 16.0m
INSTRUMENT AIR AND PLANT AIR SYSTEM	340	24.0m X 17.625m
NITROGEN SYSTEM	350	24.0m X 34.375m
NATURAL GAS FACILITIES	360	17.0m X 10.0m
AOC/ACC SYSTEM INCLUDE(U/G OSD 01 AND U/G OSD 02)	370	49.0m X 46.0m X 1.5m (D)
		34.0m X 20.0m X 1.5m (D)
EXCESS STEAM RECOVERY SYSTEM	380	17.6m X 10m
GROUND FLARE GAS SYSTEM	390	40.0m X 20.0m
IETS	400	76.0m X 46.5m
FIREWATER SYSTEM INCLUDE (FIRE FIGHTING PUMP SHED AND FIREWATER TANK)	510	21.0m X 16.5m
		ø19.0m X 23.0m (H)
EDG	520	9.0m X 2.2m
CONSUMER SUBSTATION	610	31.65m X 22.8m
SUBSTATION 2	620	40.0m X 22.0m
SUBSTATION 3	630	36.0m X 7.0m
SUBSTATION 4	640	24.15m X 13.5m
LIGHTING AND OVERALL POWER SUPPLY	650	
GROUNDING AND OVERALL LIGHTNING PROTECTION	660	
UNIT 700	700	79.3m X 68.0m
UNIT 800	800	179.0m X 66.0m
UNIT 900	900	65.0m X 53.0m

REV.	DESCRIPTION	DISP.	PRED	CHKD	REVD	APPR		DATE
			高晓龙	邢文权	梁新武			
I	ISSUED FOR DESIGN	CV	Gao Xiaolong	Xing Wenquan	Liang Xinnin			20230824
H	ISSUED FOR DESIGN	CV	Gao Xiaolong	Xing Wenquan	Liang Xinnin			20230810
G	ISSUED FOR DESIGN	CV	Gao Xiaolong	Xing Wenquan	Liang Xinnin			20230525

业主文件编号 JOB NO.	ECRF01-110-CV-DW-00-0001	页次 SHEET NO.	1 OF 1

EcoCeres EcoCeres Renewable Fuels Sdn.Bhd.(1463815-P)

中石油华东设计院有限公司
CNPC EASTCHINA DESIGN INSTITUTE CO., LTD.

EcoCeres Malaysia Renewable Fuels Project

Document Class 1

PLOT/GRADING/EARTH WORK PLAN SITE

SITE PLOT PLAN

设计阶段 DESIGN STAGE: Detail Design

比例 SCALE: 1:1000 图幅 SIZE: A1

未经CEI和EcoCeres书面许可，不得以任何方式复制或用于与本项目无关的其它用途！
Please keep confidential unless permitted by CEI and EcoCeres

会签专业 CHKD DISP. | 会签人 SIGNATURE

LEGEND:

- UNDERGROUND
- BOMBA ACCESS
- PATH OF OVERHANG
- SETBACK LINE

Notes

1. THE GENERAL PLAN MAY BE MODIFIED DUE TO BOMBA'S COMMENTS.
2. TBM 01 IS TAKEN AS THE ORIGIN OF THE LOCAL COORDINATE SYSTEM, WHICH CORRESPONDS TO THE GLOBAL COORDINATE SYSTEM BASED ON Johor Cassini Grid. THE VERTICAL DATUM IS BASED ON BM No.4004K(Jeti PLT) RL:6.73M.